


2ND ST.



SPRING ST.

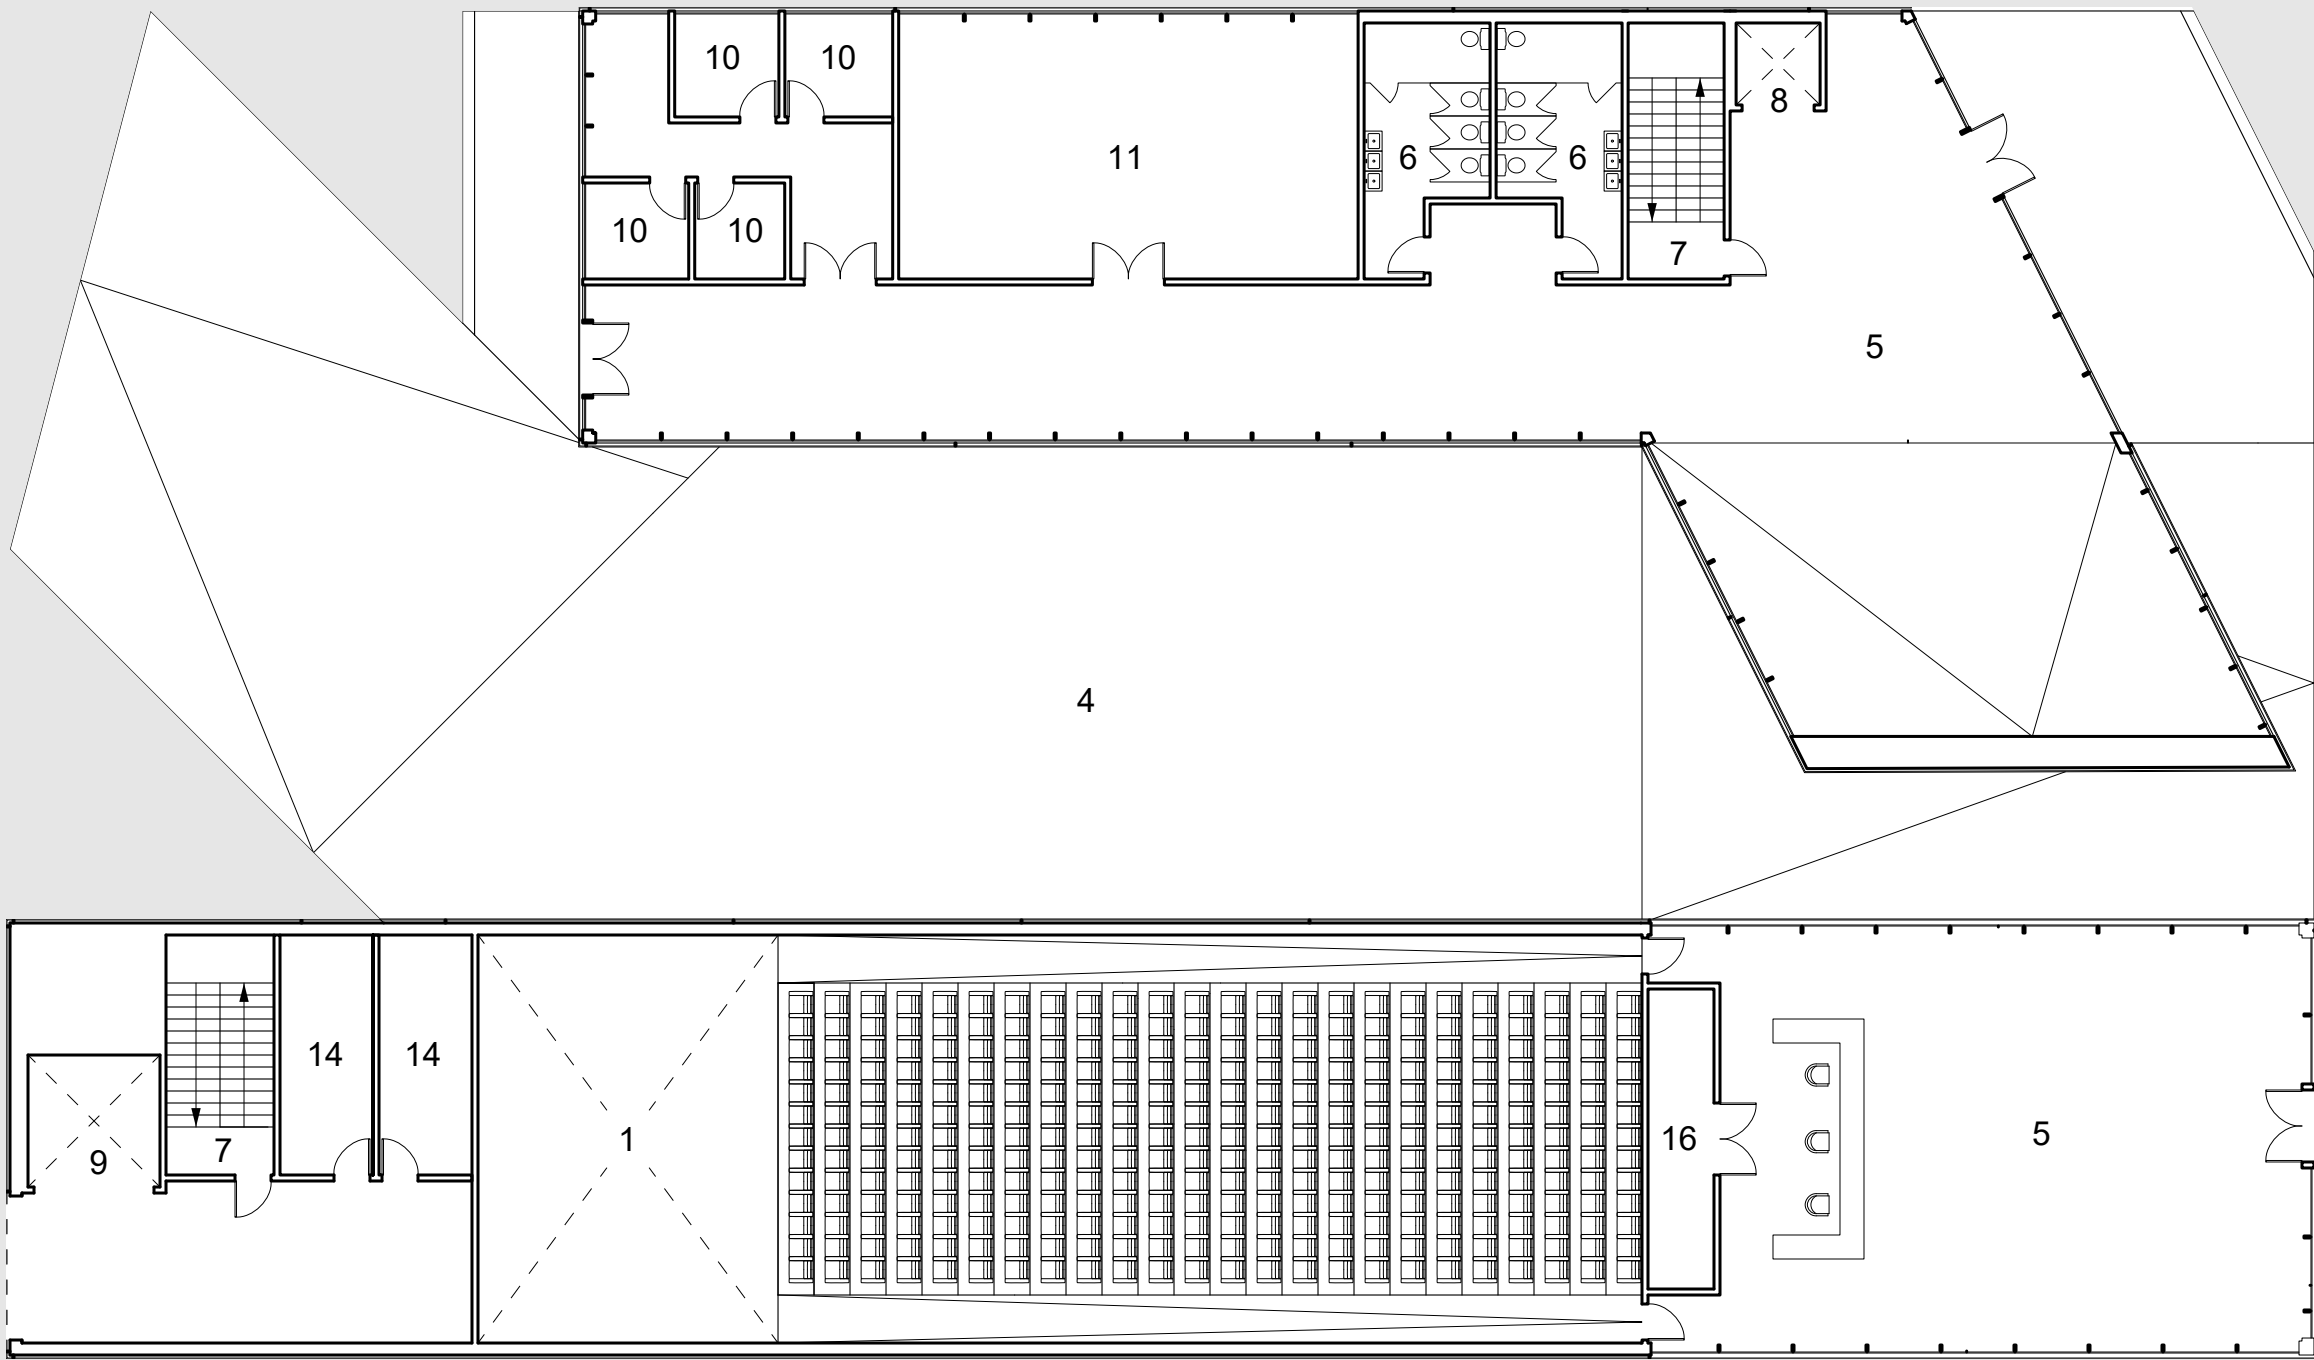